



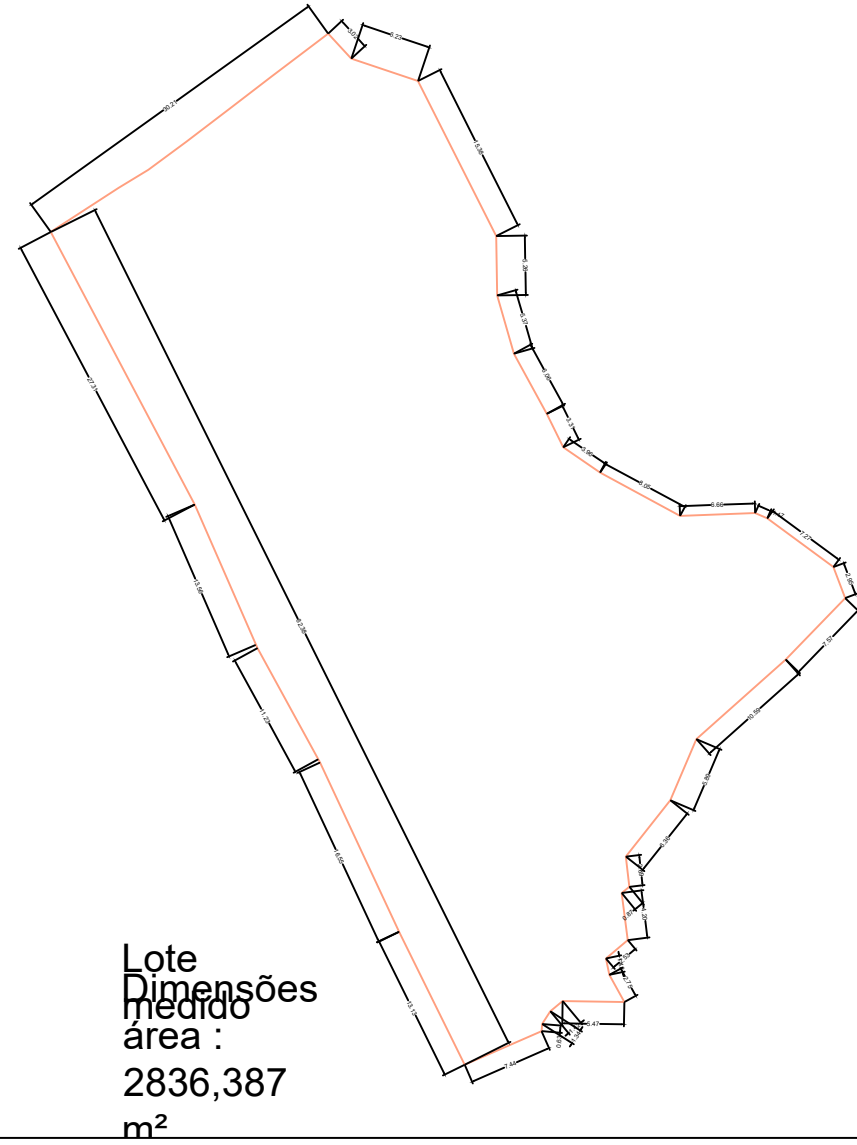

LEGENDA

	Rua		Limite Medido
	Construções		Limites na Escritura
	Geomais - Limite		Limites Vizinhos
	Curso d'água		
	APP 15 m		
	APP 30 m		
	Postes		
	Limites Vizinhos		
	Limite CACISM - GEOMAIS		

LOCALIZAÇÃO IMAGEM DE SATÉLITE (SEM ESCALA)

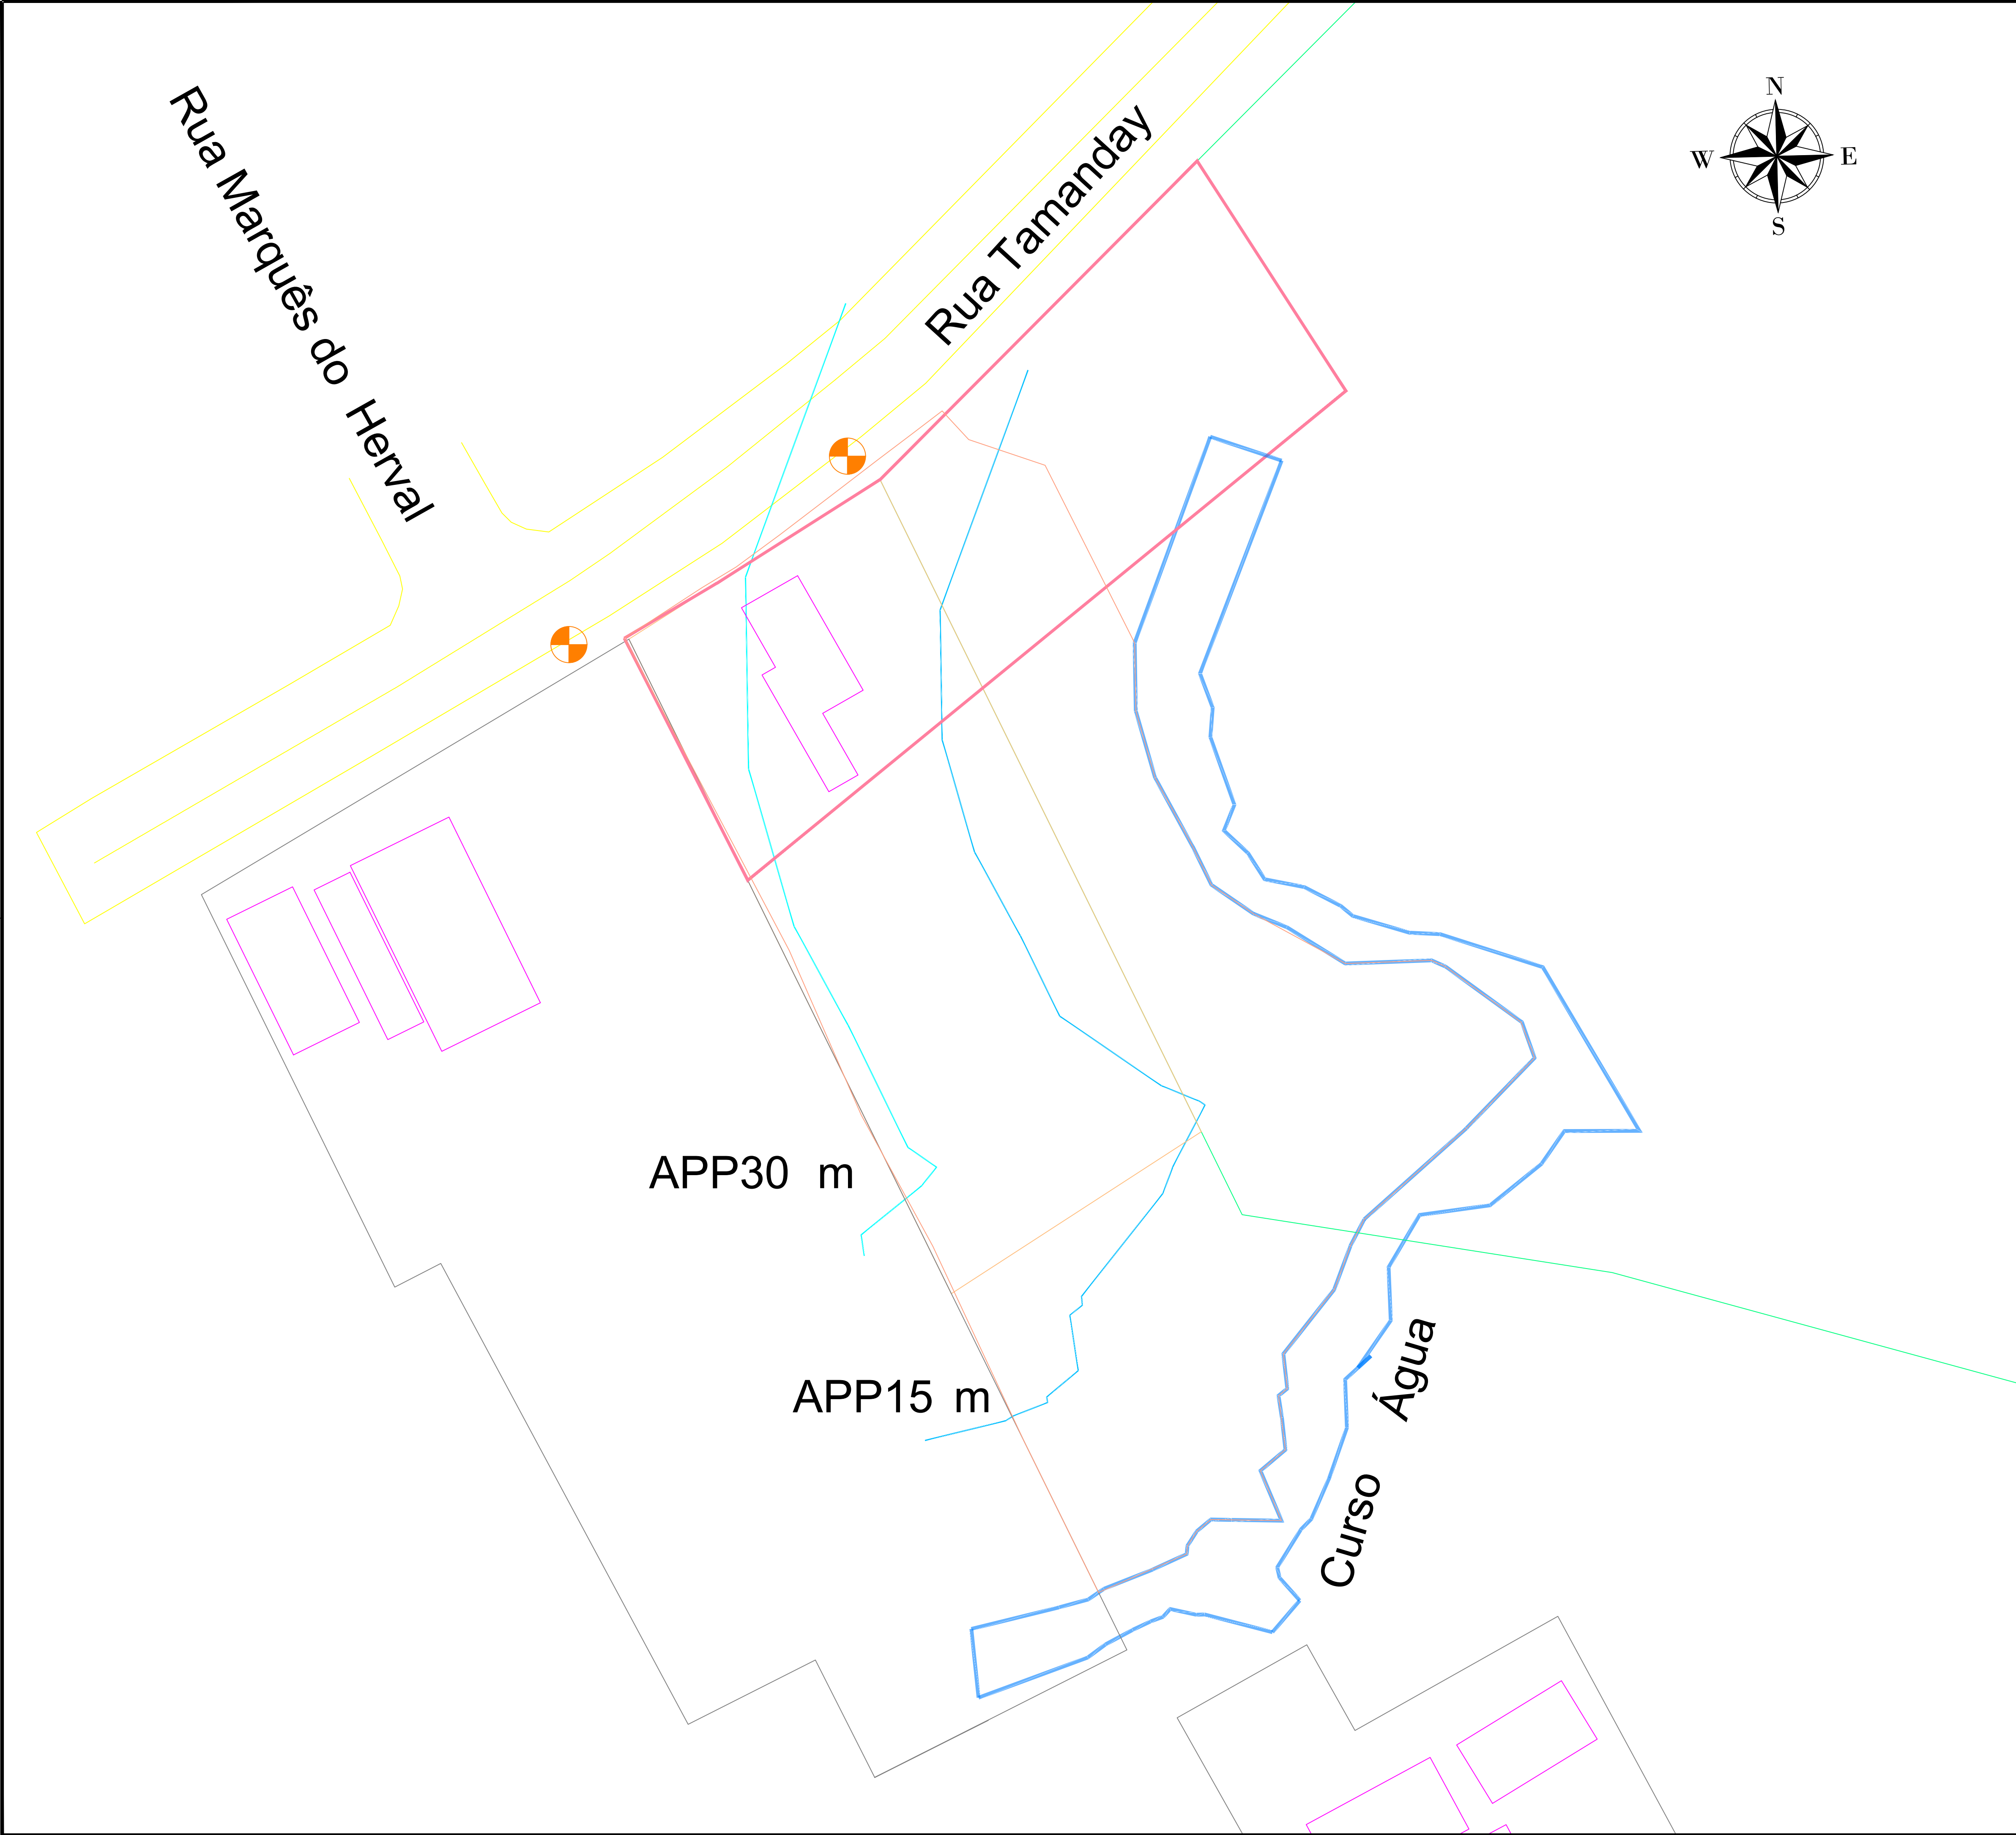

Latitude: - 29.702347°
Longitude: - 53.805098°
Datum SIRGAS 2000.

E L A B O R A Ç Ã O	Inovagro Consultoria Fone (55) 9 9669 1580 e-mail: consultorainovagro@gmail.com Rua Felipe de Oliveira, 2106, apto 02 Santa Maria/RS  INOVAGRO CONSULTORIA			
	LEVANTAMENTO PLANIALTIMÉTRICO GEORREFERENCIADO			
	LOCALIZAÇÃO RUA TAMANDAY, 632 - ZONA URBANA - SANTA MARIA - RS			
	FINALIDADE ?	ÁREA TOTAL 2864,494 m²	ART Nº ?	DATA: MARÇO/2026
	RESPONSÁVEL TÉCNICO Jonatas Giovanni Silva Almon Tecnólogo em Geoprocessamento CREA RS 308852 - Credenciado Intra CTZH Responsável Técnico		PROPRIETÁRIO: Adilson Jauer 647.407.650-04	
	ESCALA 1/1000	PRANCHA 1/1	ARQUIVO	DES. TÉC. Jonatas Almon